


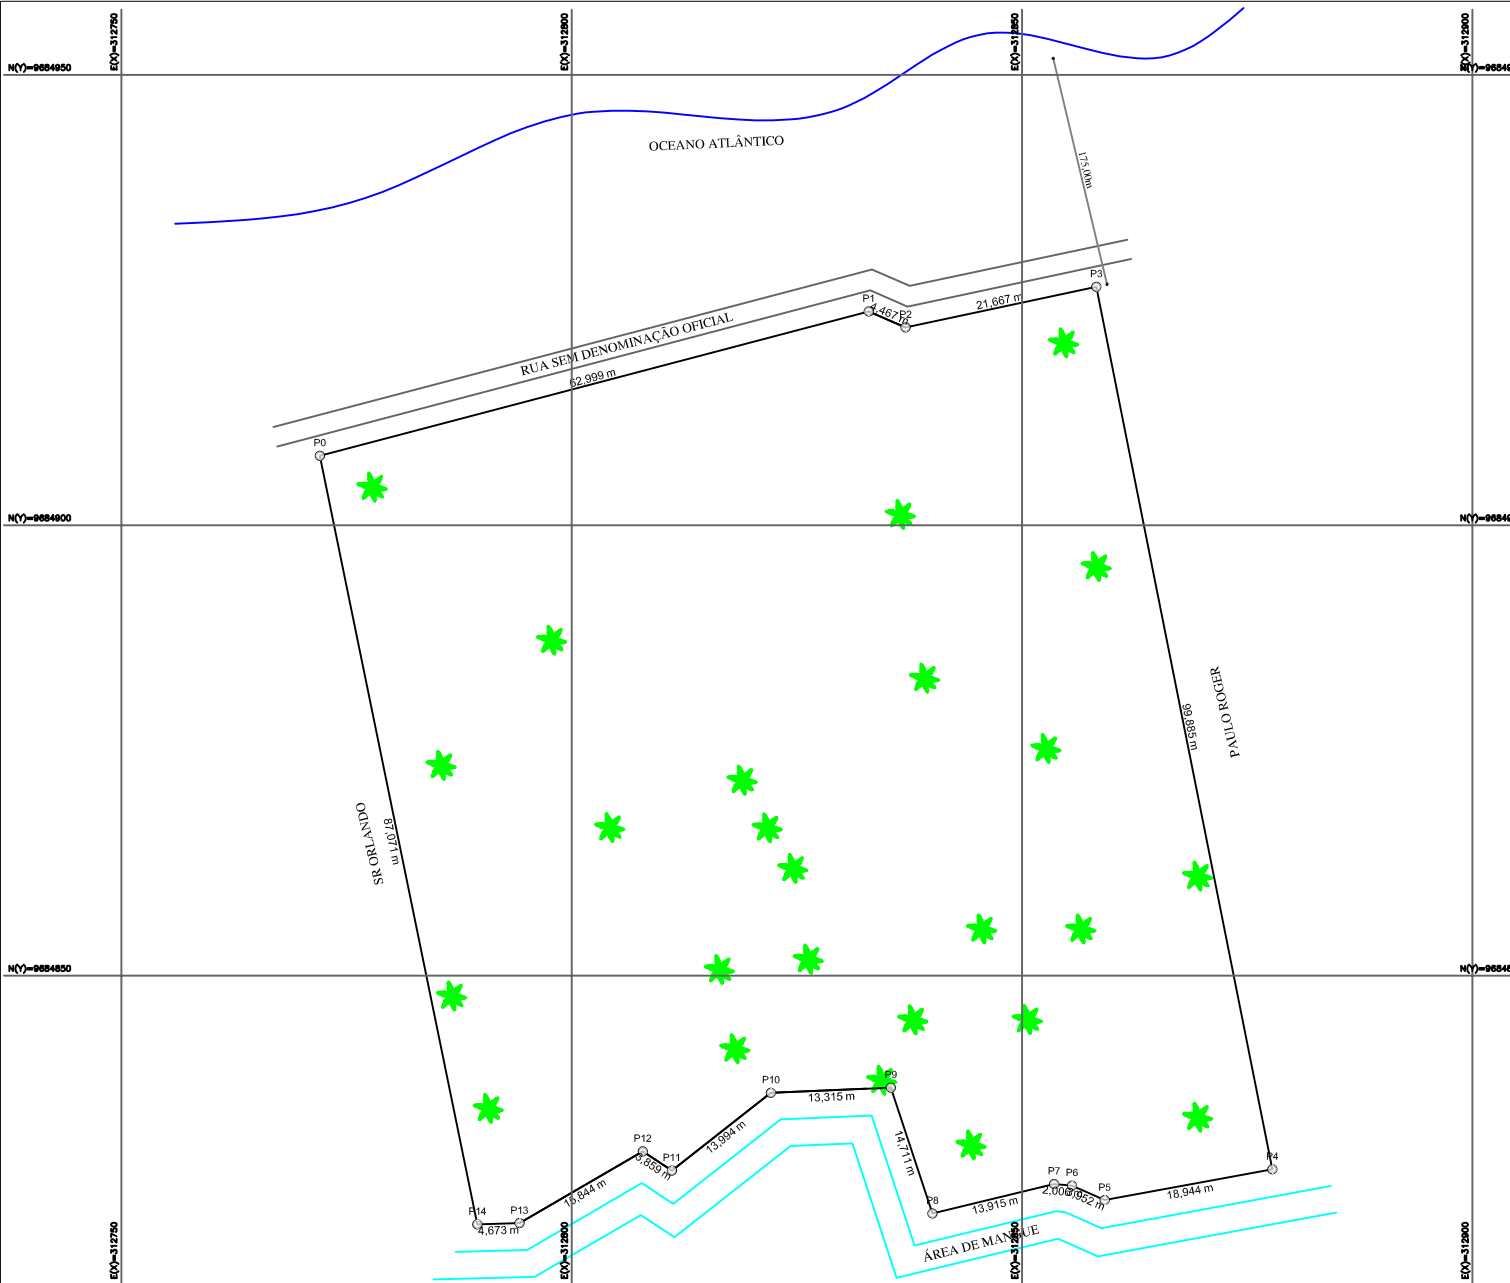

QUADRO DE ASSINATURA DOS CONFINANTES:

NOME:
CPF.:
ASS.:

NOME:
C.P.F.:
ASS.:

NOME:
CPF.:
ASS.:

QUADRO DE COORDENADAS UTM SIRGAS2000

De	Para	Coord. N(0)	Coord. E(0)	Azimuth	Ang. Int.	Distância	Latitude	Longitude
P0	P1	9.684.923.7400	312.532.9680	75°15'50"	93°08'30"	62.999 m	02°50'57.598795"S	40°41'01.853212"W
P1	P2	9.684.921.9570	312.837.0640	113°31'25"	141°44'25"	4.467 m	02°50'57.657036"S	40°41'01.720676"W
P2	P3	9.684.926.4690	312.858.2560	77°58'50"	215°32'35"	21.667 m	02°50'57.511154"S	40°41'01.034308"W
P3	P4	9.684.928.5150	312.877.8030	168°42'53"	89°15'57"	99.885 m	02°51'00.701013"S	40°41'00.406050"W
P4	P5	9.684.925.0860	312.859.1720	259°34'17"	89°08'36"	18.944 m	02°51'00.811758"S	40°41'01.009447"W
P5	P6	9.684.926.6910	312.855.5610	293°57'50"	145°36'27"	3.952 m	02°51'00.759335"S	40°41'01.126288"W
P6	P7	9.684.926.8870	312.853.5650	275°36'30"	198°21'20"	2.006 m	02°51'00.752859"S	40°41'01.190905"W
P7	P8	9.684.923.6170	312.840.0400	256°24'29"	199°12'01"	13.915 m	02°51'00.858672"S	40°41'01.628973"W
P8	P9	9.684.937.5869	312.835.4299	341°44'13"	94°40'16"	14.711 m	02°51'00.403657"S	40°41'01.777577"W
P9	P10	9.684.937.0010	312.822.1274	267°28'41"	294°15'32"	13.315 m	02°51'00.422088"S	40°41'02.208314"W
P10	P11	9.684.928.3659	312.811.1156	231°53'51"	215°34'50"	13.994 m	02°51'00.702893"S	40°41'02.585262"W
P11	P12	9.684.930.5056	312.807.9038	303°40'18"	108°13'33"	3.859 m	02°51'00.632882"S	40°41'02.669153"W
P12	P13	9.684.922.5313	312.794.2125	239°46'55"	243°53'23"	15.844 m	02°51'00.891836"S	40°41'03.112827"W
P13	P14	9.684.922.4206	312.789.5406	268°38'33"	151°08'22"	4.673 m	02°51'00.895218"S	40°41'03.264099"W
P14	P0	9.684.907.7150	312.772.0410	348°24'20"	100°14'13"	87.071 m	02°50'58.117595"S	40°41'03.826664"W

Área: 8.015,003 m²

Área: 0,8015 ha

Área: 0,3312 Alqs

Perímetro: 381,302 m

ASSUNTO: LEVANTAMENTO TOPOGRÁFICO DO IMÓVEL COM FINS DE REGULARIZAÇÃO FUNDIÁRIA

LOCAL: RUA SEM DENOMINAÇÃO OFICIAL, PRAIA DA TATAJUBA - CAMOCIM - CEARÁ

PROPRIETÁRIO: RENATO ROSSI - CPF: 287.695.248-31
ALBERTO LUIZ DE OLIVEIRA - CPF: 143.768.448-37

Ass.:

Ass.:

ÁREA TOTAL DO TERRENO: 8.015,003m²

PERÍMETRO: 381,302m

DATA:
11/05/2022

ESCALA:
1:200

RESPONSÁVEL TÉCNICO:

RANIERE REGIS DO NASCIMENTO LIMA
TÉCNICO EM AGRIMENSURA
CFT-BR nº 06322447394

PRANCHA:

01

FOLHA:

A4



CFT-BR Nº: BR20211059416

Travessa Joaquim Mota I, 67 - CAUCAIA

(85) 987465501/ raniere_regis@outlook.com

Mapa de Situação:

