


N(Y) = 9.684.500 m

N(Y) = 9.684.450 m

N(Y) = 9.684.400 m

N(Y) = 9.684.350 m

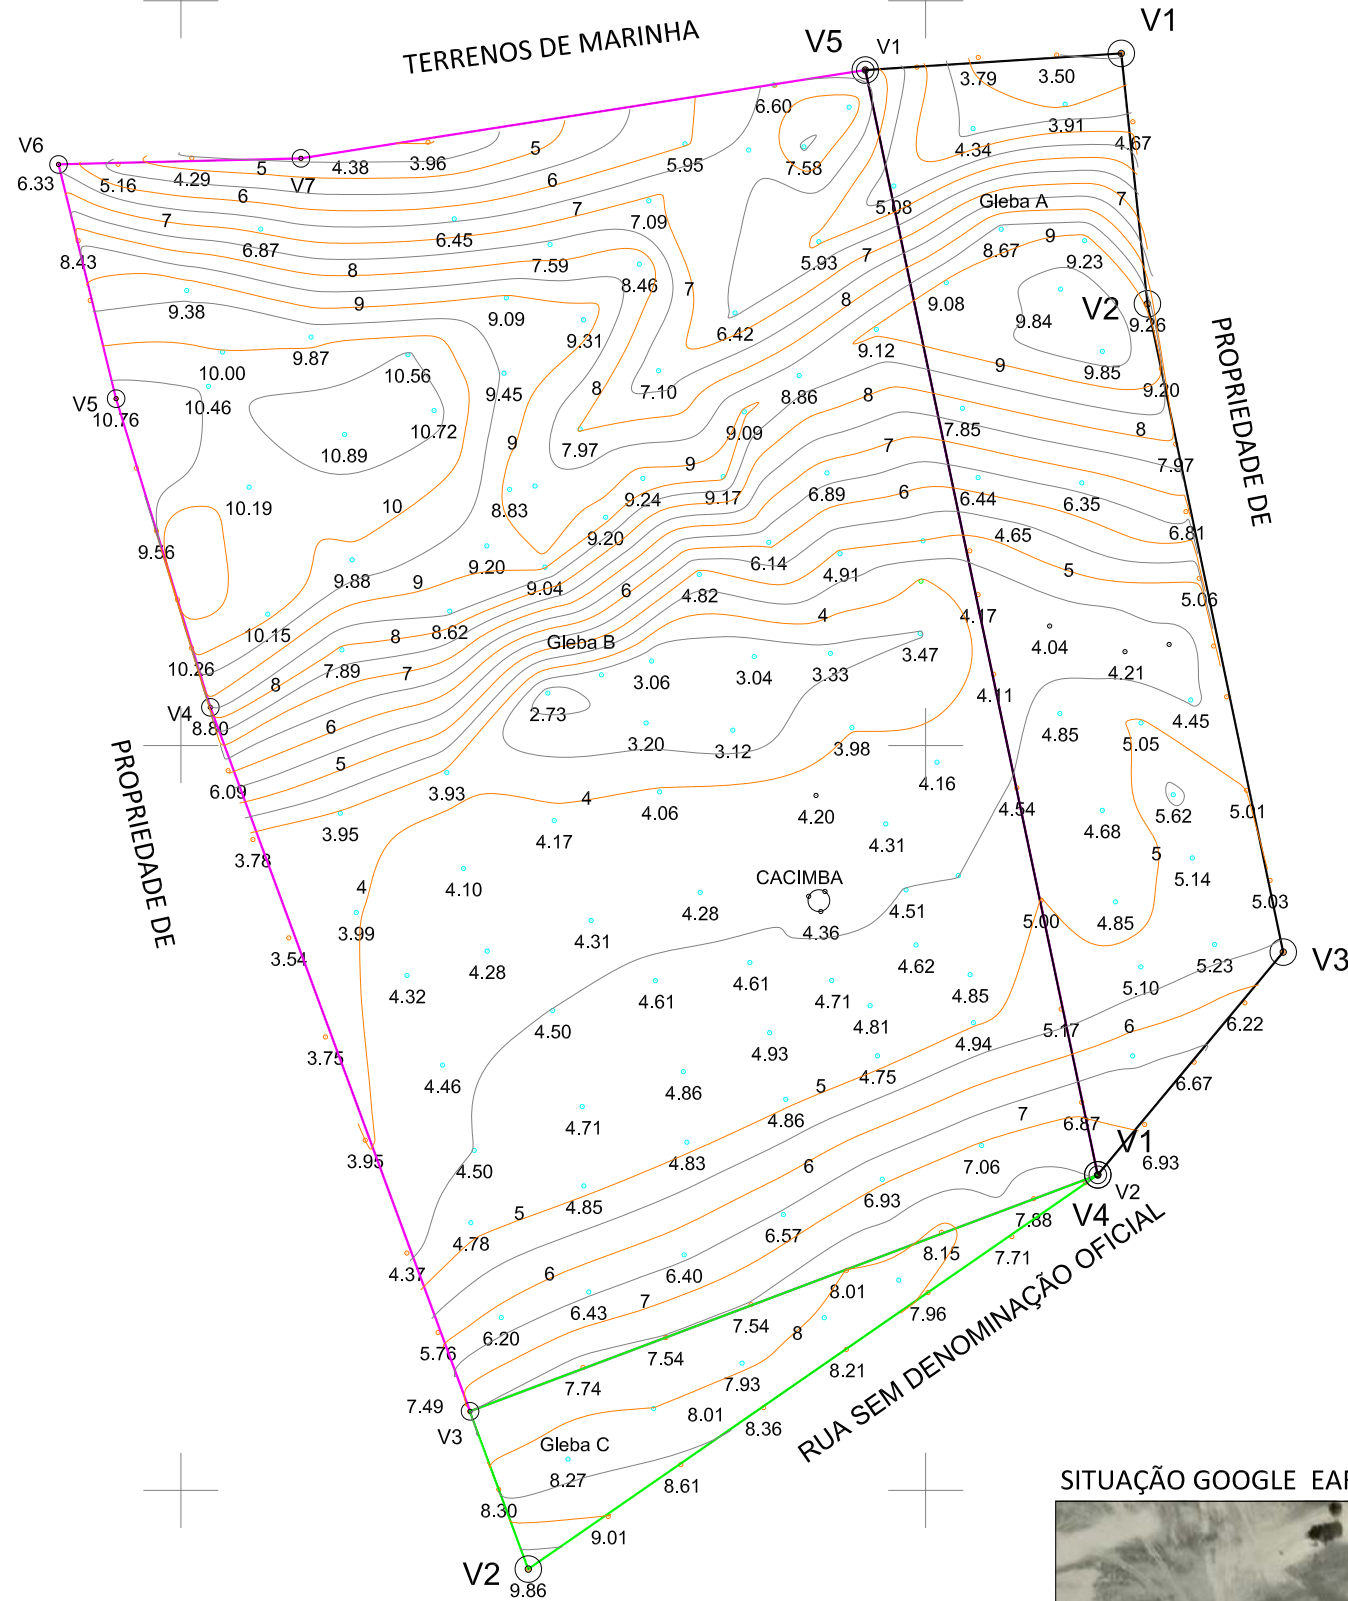


Gleba A								
De	Para	Coord. N(Y)	Coord. E(X)	Azimute	Âng. Int.	Distância	Latitude	Longitude
V1	V2	9.684.496,47	311.063,13	174°01'23"	92°14'49"	16,90 m	02°51'11,4"S	40°41'59,2"W
V2	V3	9.684.479,66	311.064,89	168°10'47"	185°50'36"	44,47 m	02°51'12,0"S	40°41'59,1"W
V3	V4	9.684.436,13	311.074,00	219°47'12"	128°23'35"	19,46 m	02°51'13,4"S	40°41'58,8"W
V4	V5	9.684.421,18	311.061,55	348°07'20"	51°39'52"	75,79 m	02°51'13,9"S	40°41'59,2"W
V5	V1	9.684.495,35	311.045,95	86°16'12"	81°51'08"	17,22 m	02°51'11,5"S	40°41'59,7"W
Área: 1.064,463 m²								
0,1064 ha								
Perímetro = 173,84 m								

Gleba B								
De	Para	Coord. N(Y)	Coord. E(X)	Azimute	Âng. Int.	Distância	Latitude	Longitude
V1	V2	9.684.495,35	311.045,95	168°07'20"	92°58'58"	75,79 m	02°51'11,5"S	40°41'59,7"W
V2	V3	9.684.421,18	311.061,55	249°21'49"	98°45'31"	45,03 m	02°51'13,9"S	40°41'59,2"W
V3	V4	9.684.405,31	311.019,41	339°45'20"	89°36'29"	50,37 m	02°51'14,4"S	40°42'0,6"W
V4	V5	9.684.452,57	311.001,98	343°00'43"	176°44'37"	21,67 m	02°51'12,9"S	40°42'1,2"W
V5	V6	9.684.473,29	310.995,65	346°12'45"	176°47'58"	16,20 m	02°51'12,2"S	40°42'1,4"W
V6	V7	9.684.489,02	310.991,79	88°35'30"	77°37'15"	16,27 m	02°51'11,7"S	40°42'1,5"W
V7	V1	9.684.489,42	311.008,06	81°06'18"	187°29'12"	38,35 m	02°51'11,7"S	40°42'1,0"W
Área: 4.086,837 m²								
0,4087 ha								
Perímetro = 263,68 m								

Gleba C								
De	Para	Coord. N(Y)	Coord. E(X)	Azimute	Âng. Int.	Distância	Latitude	Longitude
V1	V2	9.684.421,18	311.061,55	235°18'06"	14°03'32"	46,50 m	02°51'13,9"S	40°41'59,2"W
V2	V3	9.684.394,71	311.023,32	339°38'24"	75°39'42"	11,30 m	02°51'14,7"S	40°42'0,5"W
V3	V1	9.684.405,30	311.019,39	69°21'38"	90°16'46"	45,05 m	02°51'14,4"S	40°42'0,6"W
Área: 254,441 m²								
0,0254 ha								
Perímetro = 102,85 m								

SITUAÇÃO GOOGLE EARTH

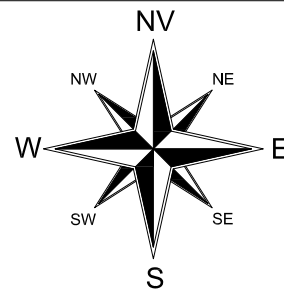

Orientação
PROJEÇÃO UNIVERSAL
TRANSVERSA DE MERCATOR - UTM
Sistema de Referência: SIRGAS 2000
Meridiano Central: 39°00' FUSO 24
DATUM VERTICAL: IMBITUBA IBGE
GPS TRIMBLE CATALYST DA2 - SISTEMA RTX

Escala Gráfica:



DECLARAÇÃO: Declaro para todos os fins e efeitos de direito que o levantamento topográfico respeitou as divisas consolidadas e o alinhamento do logradouro público, importando sujeitar-se ao que dispõe o § 14, do artigo 213, da LRP. Verificado a qualquer tempo não serem verdadeiras os fatos constantes do memorial descritivo, responderá(ão) o(a-s) o(s) requerente(s) e o profissional que o elaborou pelos prejuízos causados, independentemente das sanções disciplinares e penais. (Art. 1383, (§ único) Provimento 04/2023/CGJ-CE).

Título:

**LEVANTAMENTO PLANIALTIMÉTRICO
GEORREFERENCIADO**

Folha:

ÚNICA

Objetivo:

CONFECÇÃO DE PLANTA - REGULARIZAÇÃO FUNDIARIA

Proprietária:

LUCIANA LEITE BENEVIDES (CPF: 377.901.963-91)

Local:

**VILA DE TATAJUBA, S/N, DISTRITO DE GURIÚ,
MUNICÍPIO DE CAMOCIM, ESTADO DO CEARÁ**

Escala:

1 / 500

Data:

AGOSTO/2024

ART:

CE20241475260

Situação:

Proprietária:

LUCIANA LEITE BENEVIDES
CPF: 377.901.963-91

Resp. Técnico:

BENEDITO BERNARDINO DE FREITAS NETO
Geólogo - Técnico em Estradas e em Mineração
CREA-CE: 10.154-D / RNP: 060538517-3
Geomensor: INCR A E74

Quadro de Áreas:

LEGENDA

CACIMBA 	PONTO GEORREFERENCIADO 	CURVAS DE NIVEL
POLIGONAL - GLEBA A 	POLIGONAL - GLEBA B 	POLIGONAL - GLEBA C
	PONTO COTA 	