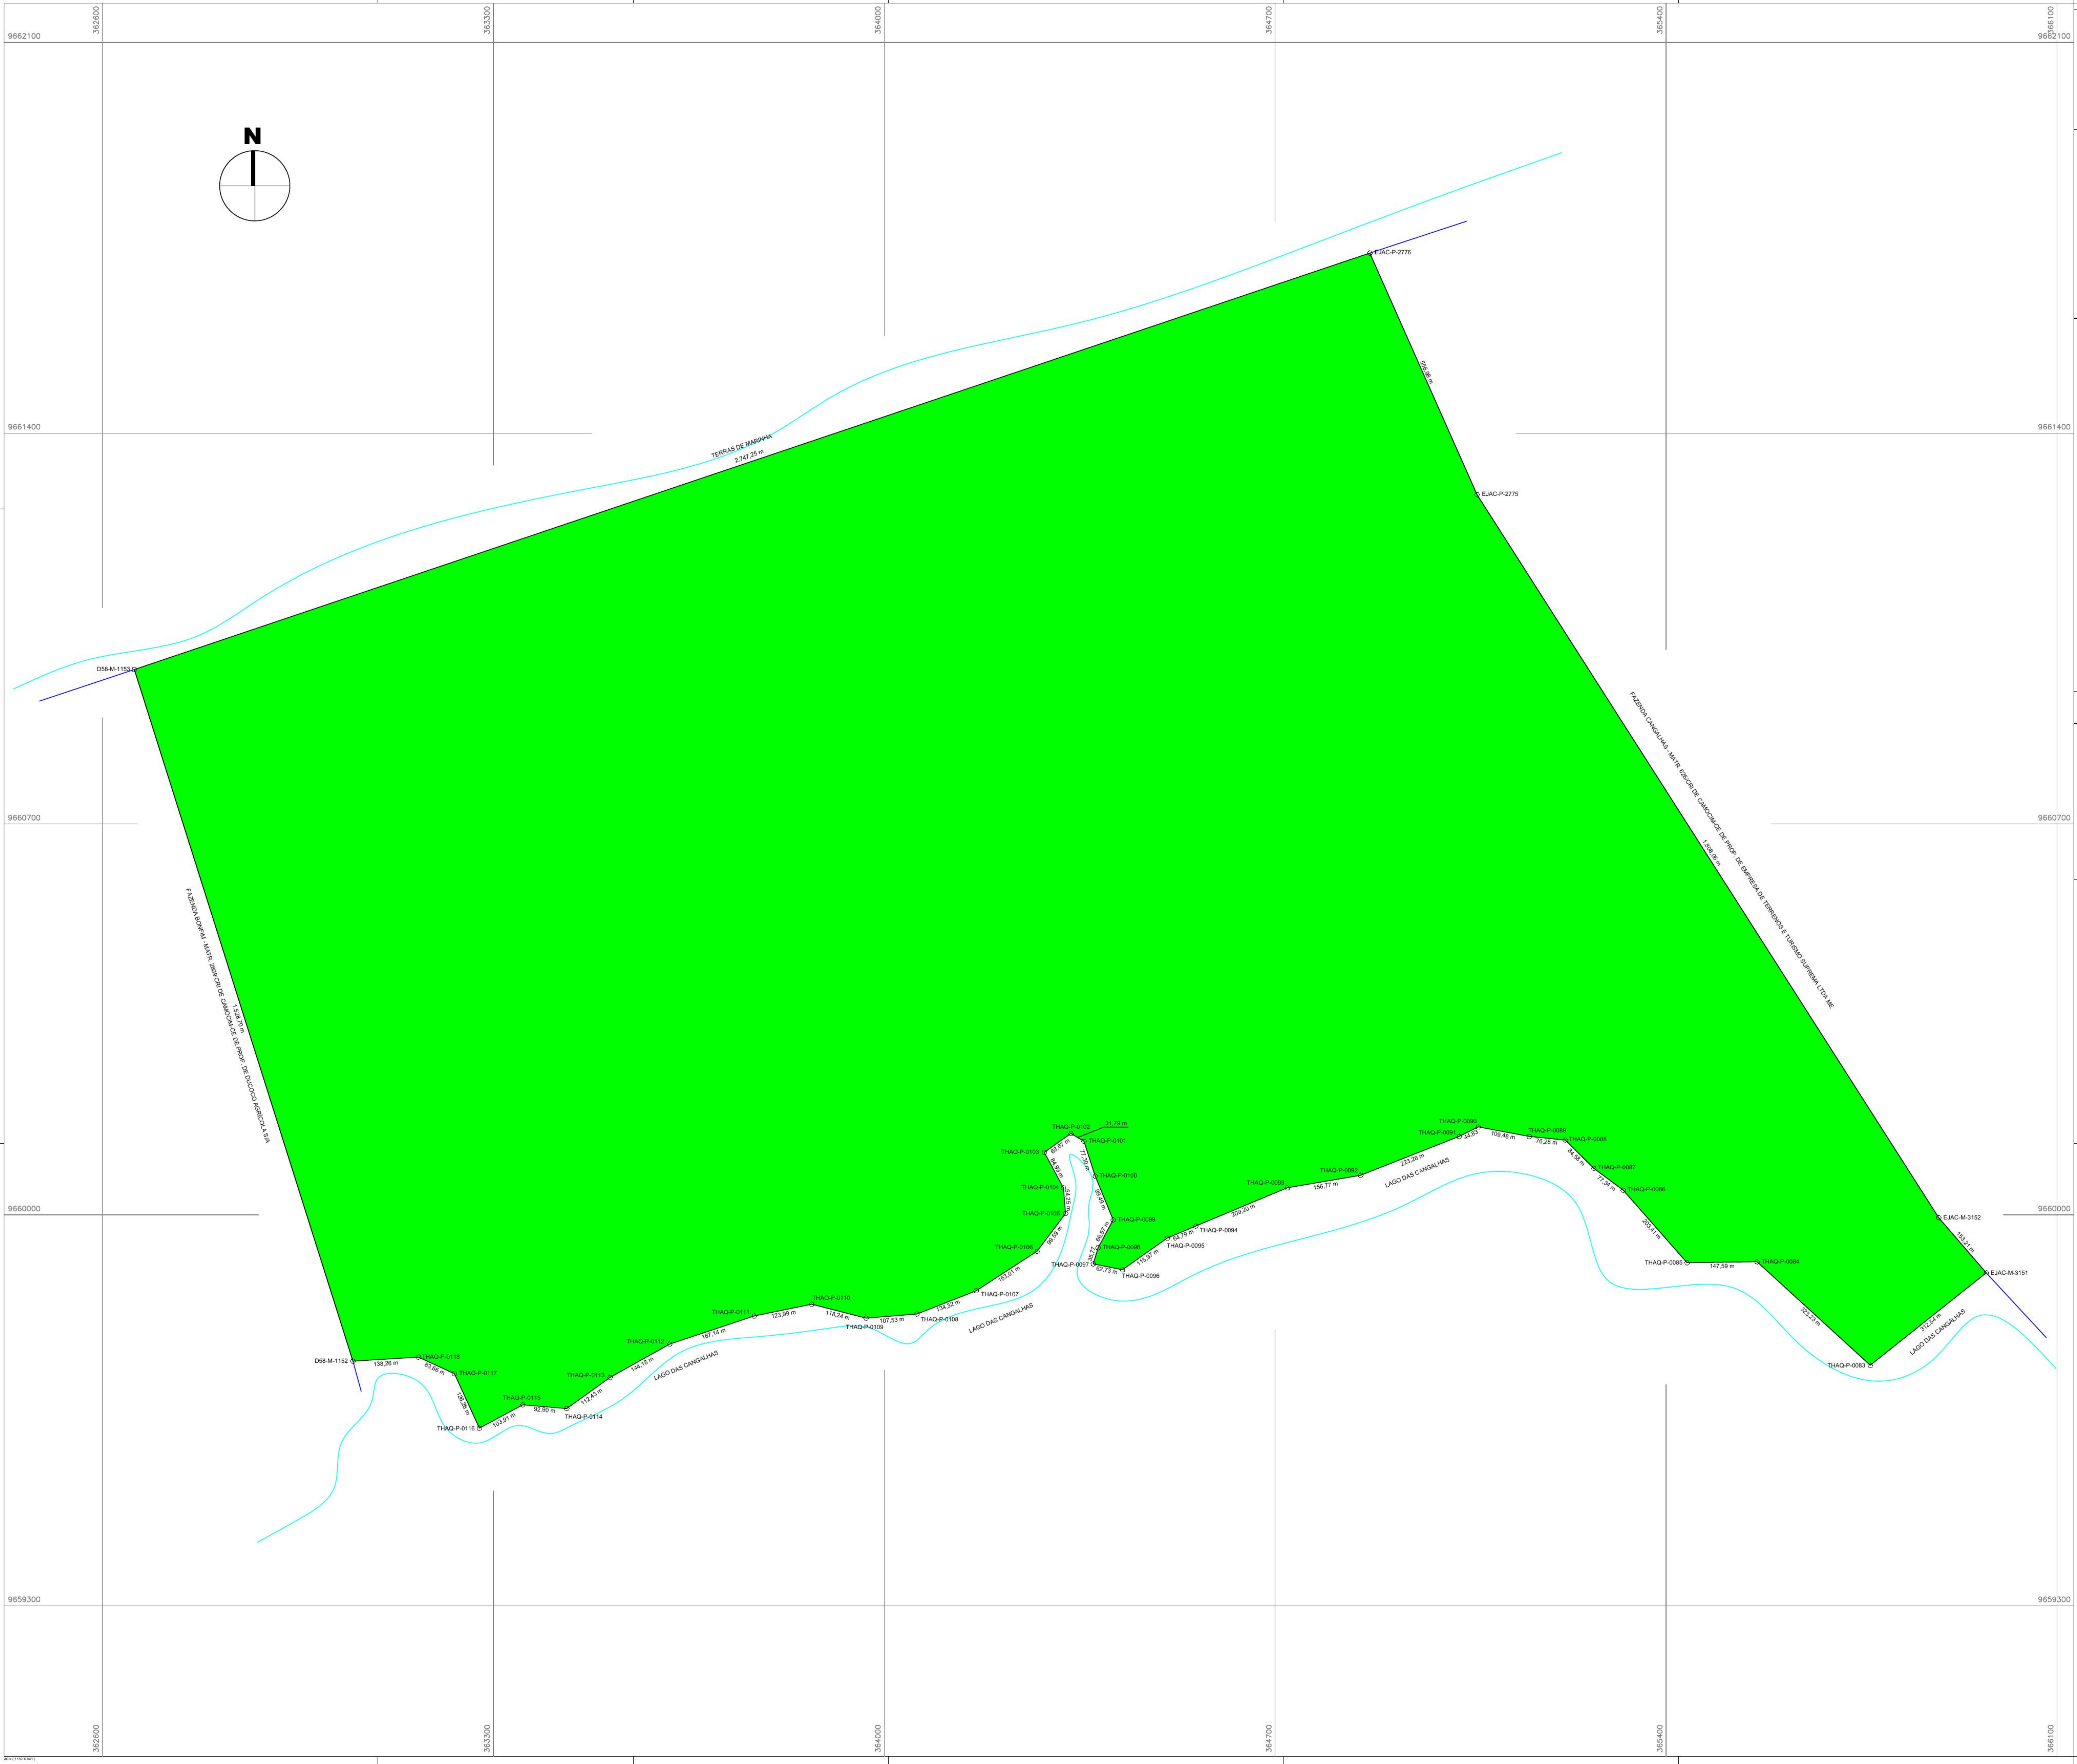
362600
363300
364000
364700
365400
366100
9662100
9661400
9660700
9660000
9659300
N
EJAC-P-2776
556,98 m
EJAC-P-2775
FAZENDA CANGALHAS - MATR. 626/CRI DE CAMOCIM-CE DE PROP. DE EMPRESA DE TERRENOS E TURISMO SUPREMA LTDA ME
1.808,06 m
EJAC-M-3152
153,21 m
EJAC-M-3151
312,54 m
LAGO DAS CANGALHAS
THAQ-P-0083
323,23 m
THAQ-P-0084
147,59 m
THAQ-P-0085
203,41 m
THAQ-P-0086
77,34 m
THAQ-P-0087
84,58 m
THAQ-P-0088
76,28 m
THAQ-P-0089
109,48 m
THAQ-P-0090
44,83
THAQ-P-0091
223,26 m
THAQ-P-0092
156,77 m
THAQ-P-0093
209,20 m
THAQ-P-0094
64,79 m
THAQ-P-0095
115,97 m
THAQ-P-0096
62,73 m
THAQ-P-0097
35,77
THAQ-P-0098
66,57 m
THAQ-P-0099
99,49 m
THAQ-P-0100
77,30 m
THAQ-P-0101
31,79 m
THAQ-P-0102
68,67 m
THAQ-P-0103
84,99 m
THAQ-P-0104
54,25 m
THAQ-P-0105
99,59 m
THAQ-P-0106
153,01 m
THAQ-P-0107
134,32 m
THAQ-P-0108
107,53 m
THAQ-P-0109
118,24 m
THAQ-P-0110
123,99 m
THAQ-P-0111
187,14 m
THAQ-P-0112
144,18 m
THAQ-P-0113
112,43 m
THAQ-P-0114
92,90 m
THAQ-P-0115
103,91 m
THAQ-P-0116
126,26 m
THAQ-P-0117
83,66 m
THAQ-P-0118
138,26 m
D58-M-1152
FAZENDA BONFIM - MATR. 2809/CRI DE CAMOCIM-CE DE PROP. DE DUCOCO AGRÍCOLA S/A
1.528,70 m
D58-M-1153
TERRAS DE MARINHA
2.747,25 m

Esse desenho foi elaborado utilizando uma versão original do sistema profissional para Cálculos, Desenhos e Projetos topográficos Métrica TOPO

A0 = (1189 X 841)

Empresa:

COSTA MENDES
ARQUITETURA & TOPOGRAFIA

Rua Emílio Fonteles, 263, Centro
Bela Cruz - CE, CEP 62570-000

(88) 99964-4782
costamendestp@gmail.com

Convenções topográficas NBR 13133

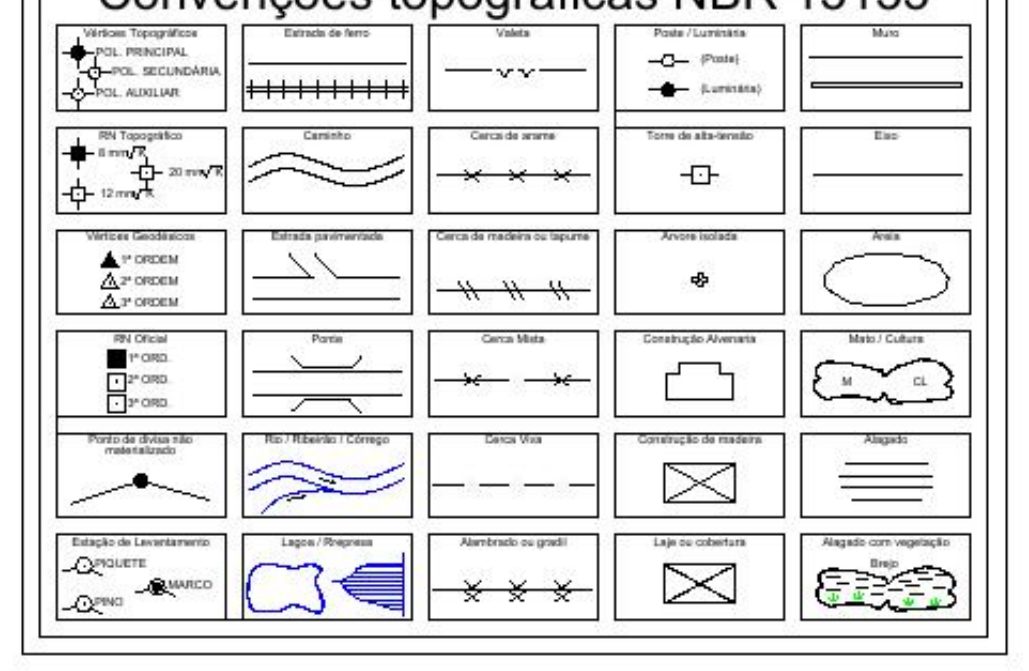
Vértices Topográficos
POL. PRINCIPAL
POL. SECUNDÁRIA
POL. AUXILIAR
Estrada de ferro
Valeta
Poste / Luminária
(Poste)
(Luminária)
Muro
RN Topográfico
Caminho
Cerca de arame
Torre de alta-tensão
Eixo
Vértices Geodésicos
1ª ORDEM
2ª ORDEM
3ª ORDEM
Estrada pavimentada
Cerca de madeira ou tapume
Árvore isolada
Areia
RN Oficial
1ª ORD.
2ª ORD.
3ª ORD.
Ponte
Cerca Mista
Construção Alvenaria
Mato / Cultura
M
CL
Ponto de divisa não materializado
Rio / Ribeirão / Córrego
Cerca Viva
Construção de madeira
Alagado
Estação de Levantamento
PIQUETE
PINO
MARCO
Lagoa / Represa
Alambrado ou gradil
Laje ou cobertura
Alagado com vegetação
Brejo

TABELA DE COORDENADAS - AZIMUTES - DISTÂNCIAS

De	Latitude	Longitude	Altitude	Azim. 3ªEd.	Dist. 3ªEd.
EJAC-P-2776	-02°53'10.784"	-40°58'59.504"	-2.78	156°09'	556.89 m
EJAC-P-2775	-02°53'27.367"	-40°58'52.215"	3.67	147°32'	1807.70 m
EJAC-M-3152	-02°54'17.027"	-40°58'20.803"	11.85	139°20'	153.18 m
EJAC-M-3151	-02°54'20.810"	-40°58'17.571"	7.88	231°31'	312.50 m
THAQ-P-0083	-02°54'27.140"	-40°58'25.493"	-9.62	312°33'	323.15 m
THAQ-P-0084	-02°54'20.024"	-40°58'33.200"	-10.74	269°18'	147.57 m
THAQ-P-0085	-02°54'20.082"	-40°58'37.978"	-10.51	318°44'	203.37 m
THAQ-P-0086	-02°54'15.104"	-40°58'42.320"	-10.87	306°46'	77.33 m
THAQ-P-0087	-02°54'13.597"	-40°58'44.326"	-4.66	314°49'	84.57 m
THAQ-P-0088	-02°54'11.656"	-40°58'46.268"	-0.87	275°56'	76.26 m
THAQ-P-0089	-02°54'11.399"	-40°58'48.724"	-5.88	280°39'	109.45 m
THAQ-P-0090	-02°54'10.740"	-40°58'52.207"	-10.89	243°37'	44.81 m
THAQ-P-0091	-02°54'11.388"	-40°58'53.507"	-10.56	248°33'	223.22 m
THAQ-P-0092	-02°54'14.044"	-40°59'00.235"	-10.69	260°25'	156.72 m
THAQ-P-0093	-02°54'14.893"	-40°59'05.239"	-10.78	247°26'	209.18 m
THAQ-P-0094	-02°54'17.506"	-40°59'11.494"	-10.74	247°05'	64.78 m
THAQ-P-0095	-02°54'18.327"	-40°59'13.426"	-10.78	234°55'	115.95 m
THAQ-P-0096	-02°54'20.496"	-40°59'16.499"	-10.77	281°26'	62.70 m
THAQ-P-0097	-02°54'20.091"	-40°59'18.489"	-10.55	17°01'	35.75 m
THAQ-P-0098	-02°54'18.978"	-40°59'18.150"	-10.77	28°21'	66.57 m
THAQ-P-0099	-02°54'17.071"	-40°59'17.126"	-10.11	337°47'	99.46 m
THAQ-P-0100	-02°54'14.073"	-40°59'18.343"	-10.71	342°06'	77.30 m
THAQ-P-0101	-02°54'11.678"	-40°59'19.112"	-10.71	301°00'	31.78 m
THAQ-P-0102	-02°54'11.145"	-40°59'19.994"	-10.77	234°54'	68.66 m
THAQ-P-0103	-02°54'12.430"	-40°59'21.813"	-10.75	151°51'	84.99 m
THAQ-P-0104	-02°54'14.870"	-40°59'20.515"	-10.72	175°21'	54.21 m
THAQ-P-0105	-02°54'16.629"	-40°59'20.373"	-10.88	217°04'	99.57 m
THAQ-P-0106	-02°54'19.215"	-40°59'22.317"	-10.64	237°05'	152.99 m
THAQ-P-0107	-02°54'21.921"	-40°59'26.476"	-10.80	248°39'	134.28 m
THAQ-P-0108	-02°54'23.512"	-40°59'30.526"	-10.69	265°28'	107.50 m
THAQ-P-0109	-02°54'23.788"	-40°59'33.996"	-10.88	284°30'	118.22 m
THAQ-P-0110	-02°54'22.824"	-40°59'37.702"	-10.82	258°29'	123.95 m
THAQ-P-0111	-02°54'23.629"	-40°59'41.635"	-10.78	251°41'	187.10 m
THAQ-P-0112	-02°54'25.542"	-40°59'47.387"	-10.60	240°55'	144.14 m
THAQ-P-0113	-02°54'27.823"	-40°59'51.466"	-10.61	234°23'	112.41 m
THAQ-P-0114	-02°54'29.954"	-40°59'54.425"	-10.79	274°59'	92.88 m
THAQ-P-0115	-02°54'29.691"	-40°59'57.421"	-10.72	241°48'	103.89 m
THAQ-P-0116	-02°54'31.289"	-41°00'00.386"	-10.42	335°33'	126.25 m
THAQ-P-0117	-02°54'27.547"	-41°00'02.077"	-10.97	294°47'	83.65 m
THAQ-P-0118	-02°54'26.405"	-41°00'04.536"	-10.14	266°35'	138.23 m
D58-M-1152	-02°54'26.673"	-41°00'09.004"	12.96	342°33'	1528.39 m
D58-M-1153	-02°53'39.200"	-41°00'23.832"	3.24	71°28'	2746.67 m

ESCALA:

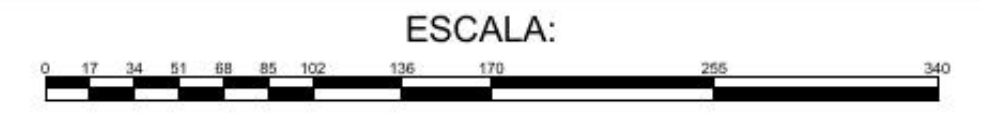
0
17
34
51
68
85
102
136
170
255
340

LEGENDA

	Córrego ou Nascente
	Rodovias
	Vias de Acesso
	Área de Preservação
CRED-M-0001	Marcos Implantados
CRED-P-0001	Pontos Levantados
CRED-V-0001	Vértices Virtuais

Informações de Coordenadas
PROJEÇÃO UNIVERSAL TRANSVERSA DE MERCATOR - UTM
SGR -SIRGAS2000
MC: 39°

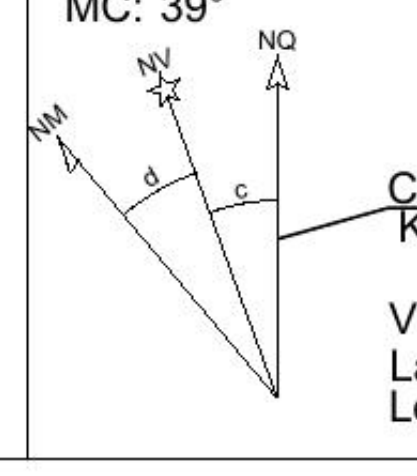

CM 00°03'52.526537"
K: 0.999822921

VÉRTICE:THAQ-P-0011
Lat.: 03°03'55.816" S
Long.: 40°12'27.454" W

Planta de Situação:

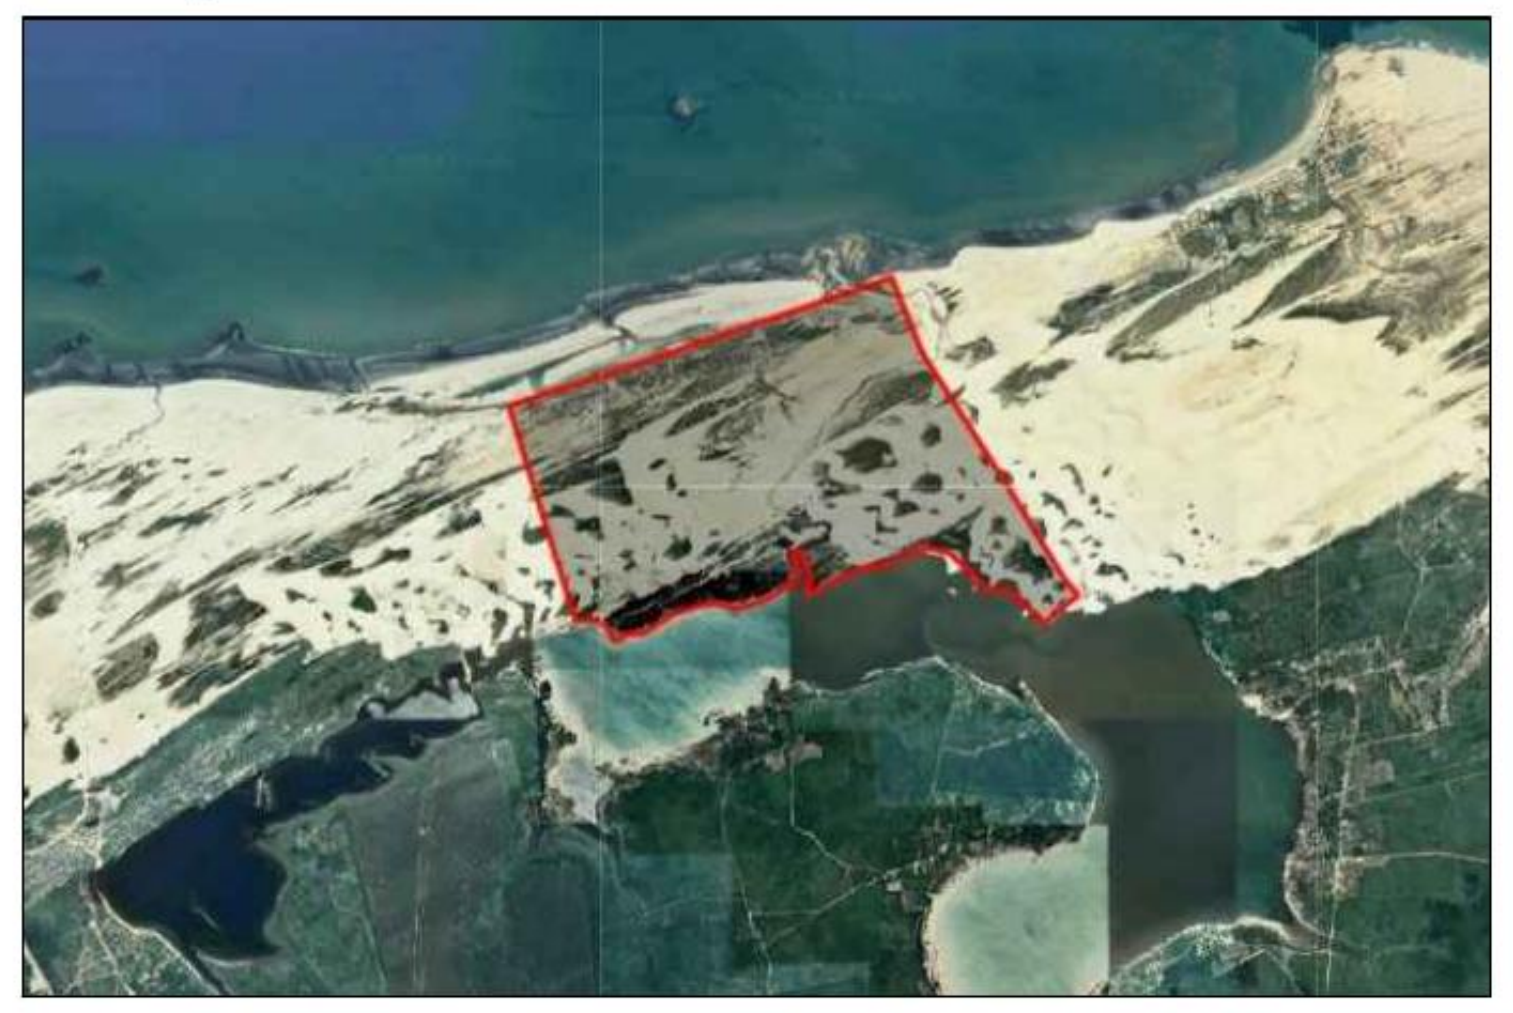

Título:

Levantamento Planialtimétrico

Folha:
01

PROPRIEDADE: SÍTIO ESPINHO
PROPRIETÁRIO: ADALGISA BEZERRA DA SILVA
PROPRIETÁRIO: HYDROFUEL IND. E COMERCIO DE EQUIPAMENTOS DE PRODUCAO DE OXI-HIDROGENIO, PROD. E DIST. DE ENERGIAS ALTERNATIVAS E EMPREEND IMOBILIARIOS LTDA
MUNICÍPIO/COMARCA: Camocim
CÓDIGO INCRA: 1410380061578
MAT./TRANSC.: 783 CNS: 01.621-2
CERTIF. SIGEF: 65466328-02f5-45f7-8d74-072f81c39e10
ÁREA TOTAL (ha): 549,0392 ha PERÍMETRO (m): 11.248,10 m
DATA: 27/09/24 ESCALA: 1 / 5000

Quadro de Áreas e Perímetros:

Matrícula 783

Área Total: 549,0392 ha
Perímetro Total: 11.248,10 m

Quadro de Assinaturas:

Prop.:
ADALGISA BEZERRA DA SILVA
CPF: OMITIDO

Prop.:
HYDROFUEL IND. E COMERCIO DE EQUIPAMENTOS DE PRODUCAO DE OXI-HIDROGENIO, PROD. E DIST. DE ENERGIAS ALTERNATIVAS E EMPREEND IMOBILIARIOS LTDA
CNPJ: 10.512.404/0001-18

Resp. Téc.:
JOSÉ TADEU COSTA MENDES
Tecnólogo Gestão Ambiental
Téc. Edificações / Agrimensura
CREA: 357750CE | CFT/CRT02: 39010473368
DOC. RT: CFT2403888198 - CE

"Declaro para todos os fins e efeitos de direito que o levantamento topográfico respeitou as divisas consolidadas e o alinhamento do logradouro público, importando sujeitar-se ao que dispõe o parágrafo 14, do artigo 213, da LRP. Verificado a qualquer tempo não serem verdadeiros os fatos constantes do memorial descritivo, responderão o requerente e o profissional que o elaborou pelos prejuízos causados independentemente das sanções disciplinares e penais"