


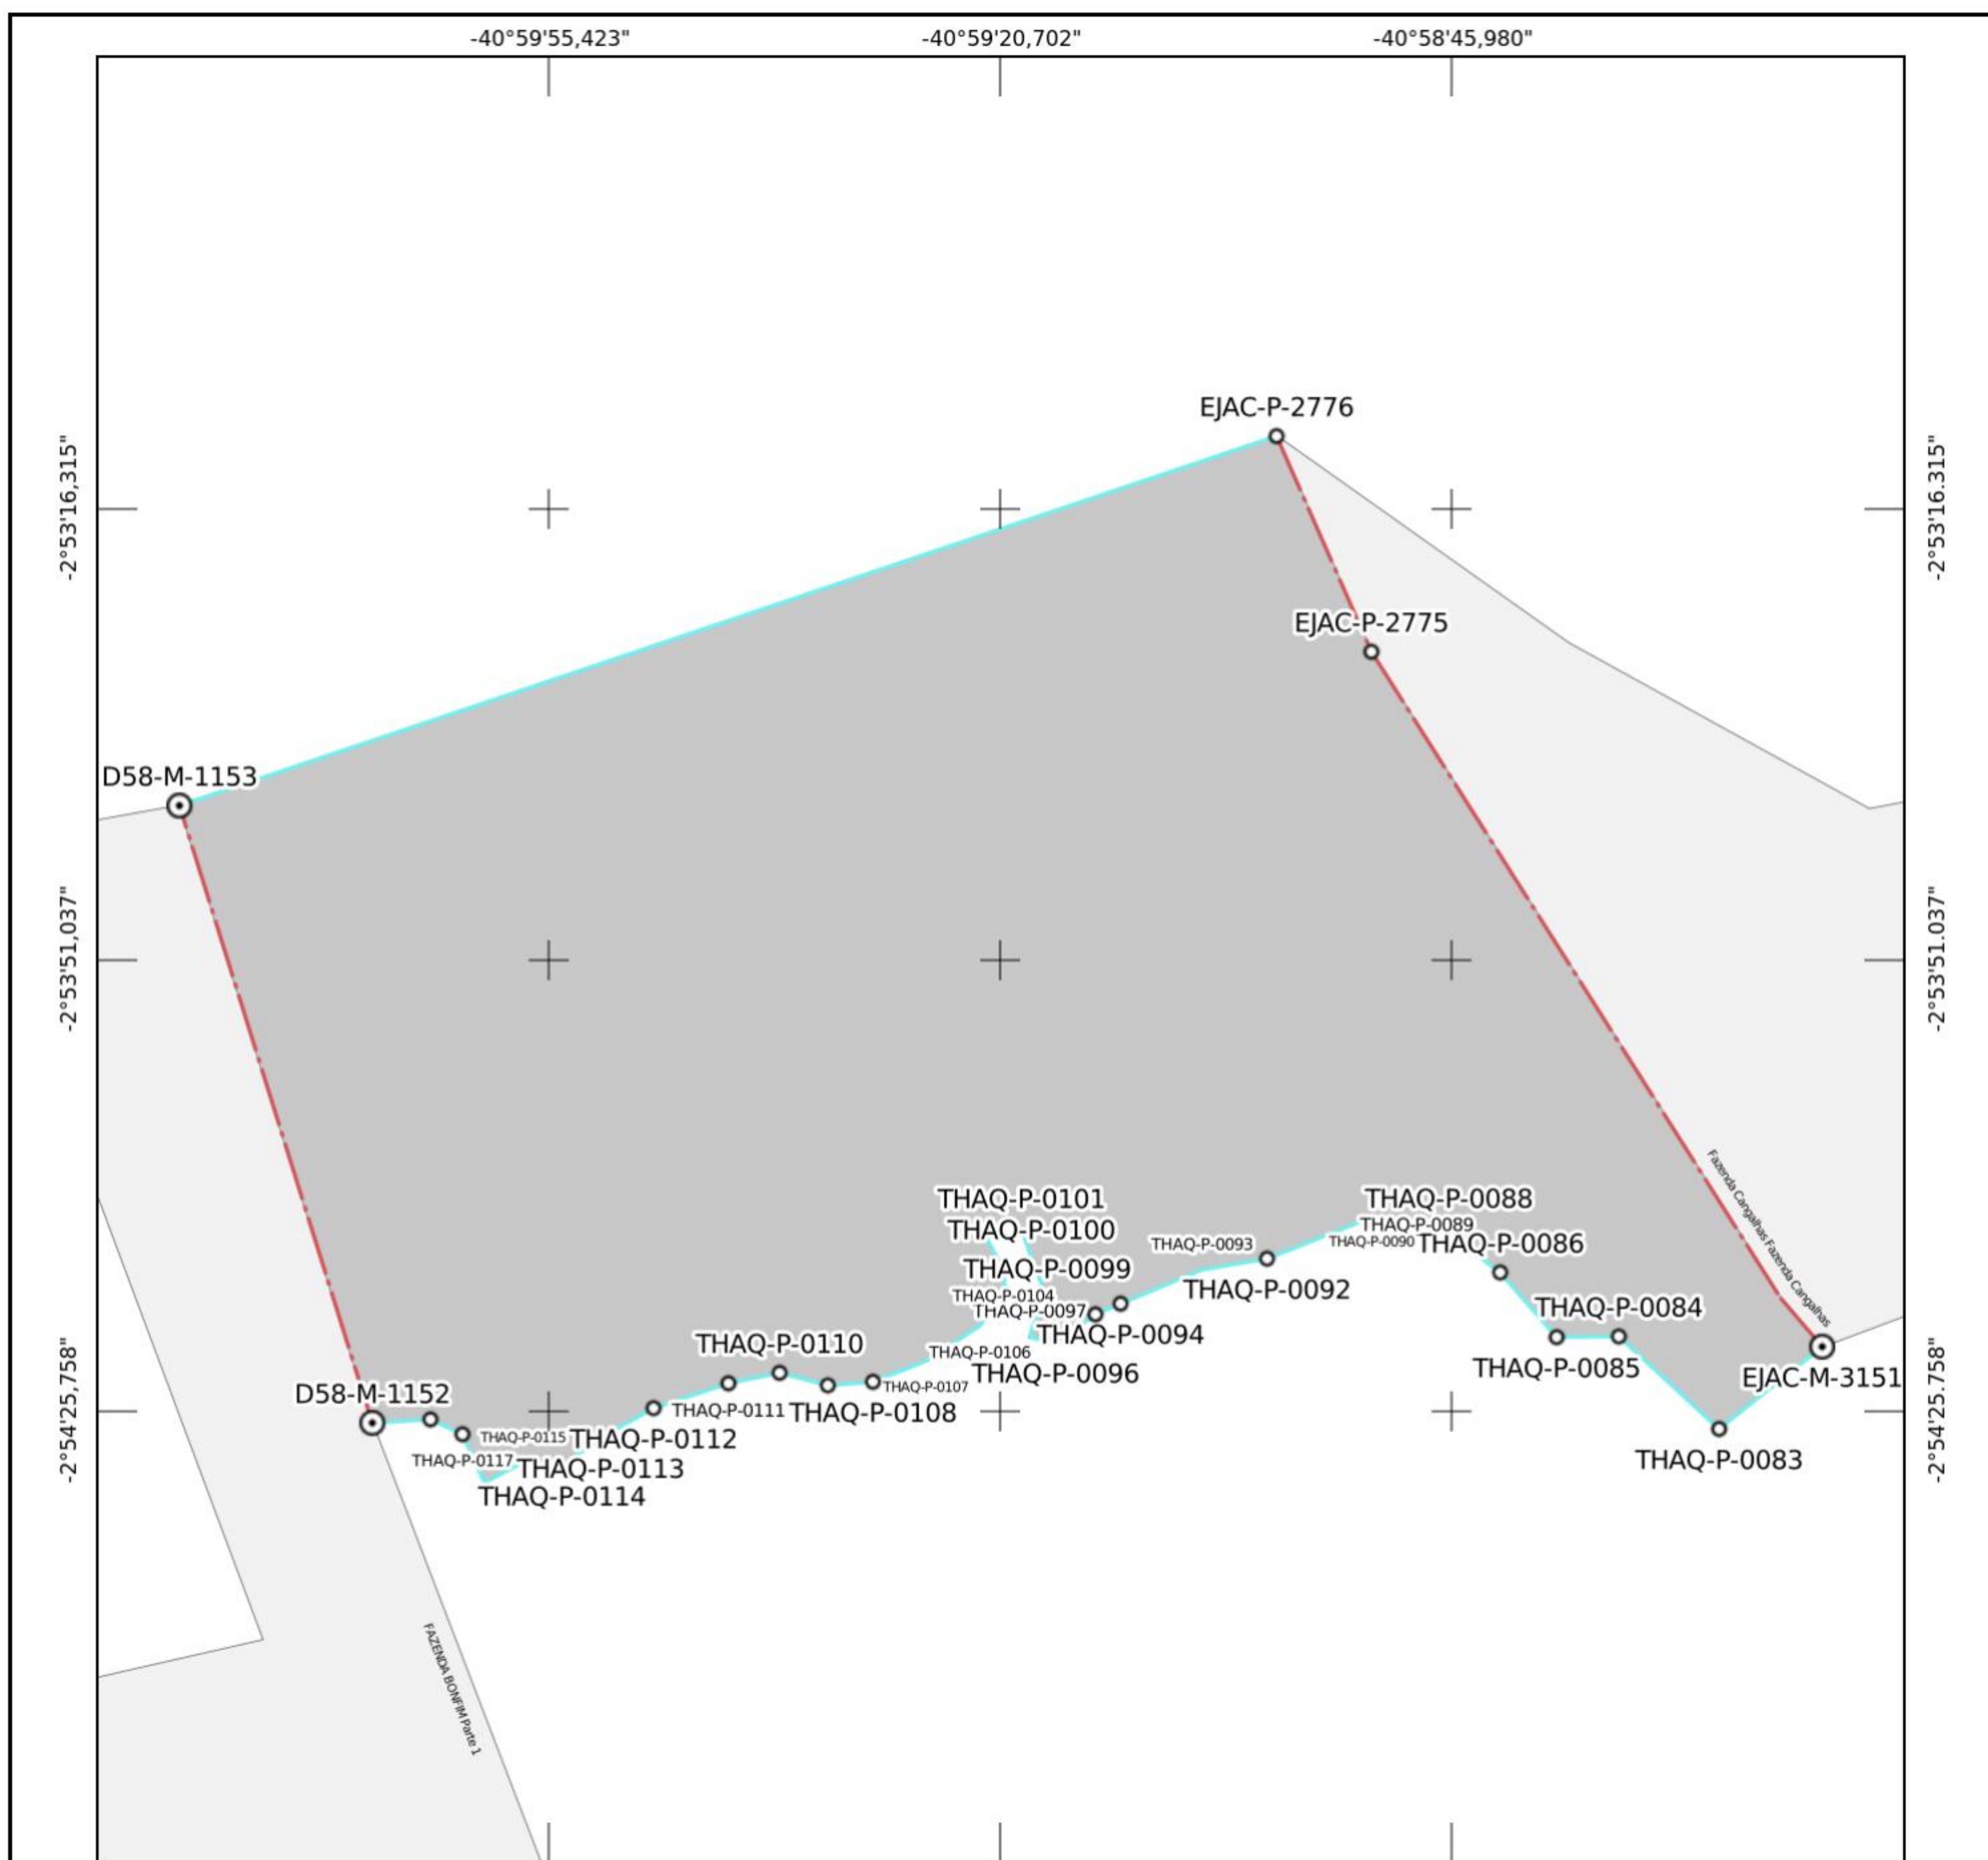

Certificada - Sem Confirmação de Registro em Cartório

Parcela certificada pelo SIGEF de acordo com a Lei 6.015/73 e pendente de confirmação do registro da certificação em cartório



MINISTÉRIO DA AGRICULTURA, PECUÁRIA E ABASTECIMENTO

INSTITUTO NACIONAL DE COLONIZAÇÃO E REFORMA AGRÁRIA



Denominação:

SÍTIO ESPINHO

Proprietário(a):

ADALGISA BEZERRA DA SILVA ... e outros

CPF: OMITIDO

Matrícula do imóvel:

783

Cartório de Registro de Imóveis:

(01.621-2) Camocim - CE

Código INCRA/SNCR:

1410380061578

Município:

Camocim-CE

Natureza da Área:

Particular

Responsável Técnico(a):

JOSE TADEU COSTA MENDES

Formação:

Técnico(a) Industrial em Agrimensura

Conselho Profissional:

39010473368/CE

Cód. Credenciado(a):

THAQ

Documento de RT:

CFT2403888198 - CE

Área (Sistema Geodésico Local):

549,0392 ha

Perímetro:

11.248,10 m

Sistema Geodésico:

SIRGAS 2000

Sistema de Coordenadas:

Lat./Long. - não projetado

Escala:

1:24753

Formato:

A0

⊙	Vértice tipo M	---	Linha ideal	—*—*	Cerca
○	Vértice tipo P	---	Limite artificial não tipificado		
•	Vértice tipo V	---	Corpo d'água ou curso d'água		
●	Vértice tipo O	---	Linha de cumeada		
—+—+	Muro	---	Grota	■	Imóvel em estudo
—+—+	Estrada	---	Crista de encosta	□	Imóveis confrontantes
—+—+	Vala	---	Pé de encosta		
—+—+	Canal	---	Limite natural não tipificado		

CERTIFICAÇÃO: 65466328-02f5-45f7-8d74-072f81c39e10

Em atendimento ao § 5º do art. 176 da Lei 6.015/73, certificamos que a poligonal objeto deste memorial descritivo não se sobrepõe, nesta data, a nenhuma outra poligonal constante do cadastro georreferenciado do INCRA.

Data Certificação: 27/09/24 22:07

Data da Geração: 27/09/24 22:11

